



REPUBLIKA E KOSOVËS / REPUBLIKA KOSOVA / REPUBLIC OF KOSOVO
QEVERTA E KOSOVËS / VLADA KOSOVA / GOVERNMENT OF KOSOVA

MINISTRIA E EKONOMISË DHE AMBIENTIT / MINISTARSTVO EKONOMIJE I ŽIVOTNE SREDINE / MINISTRY OF ECONOMY AND ENVIRONMENT


AGJENCIA KADASTRALE E KOSOVËS / KATASTARSKA AGENCIJA KOSOVA / KOSOVA CADASTRAL AGENCY

Rapor i njësisë kadastrale

Zonë kadastrale: Rahovicë

Lloji i njësisë kadastrale: Parcelë

Nr i njësisë kadastrale: P-72217072-01949-1

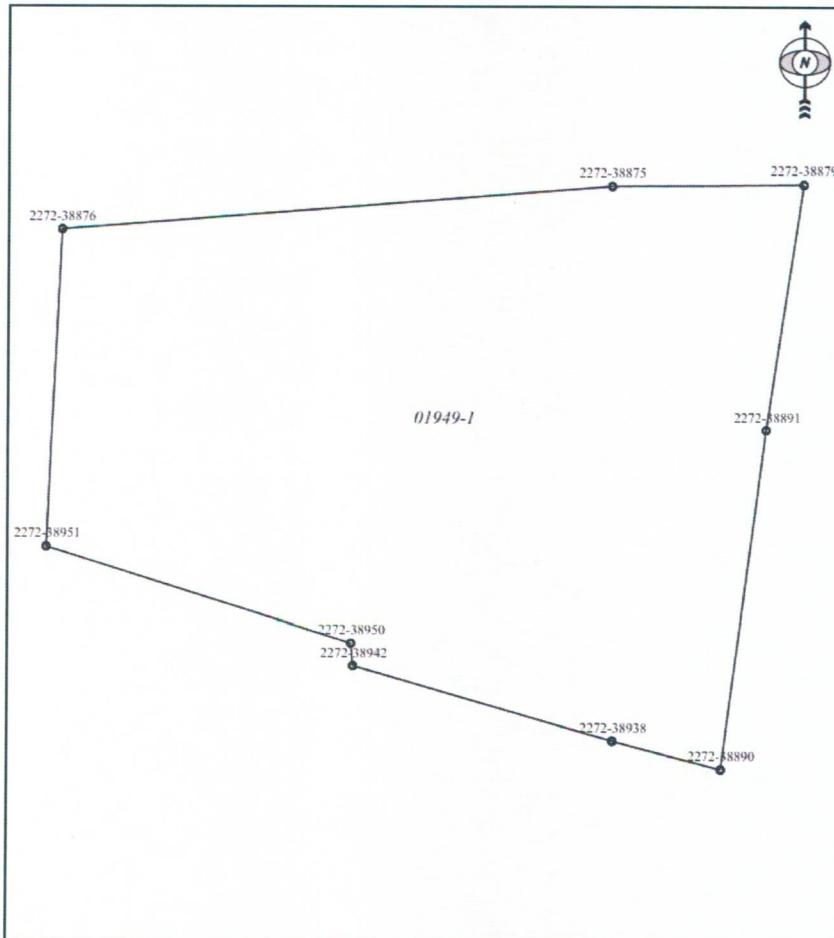

Pika	Y	X
2272-38890	7519013.766	4698238.238
2272-38938	7519004.914	4698240.543
2272-38942	7518983.720	4698246.630
2272-38950	7518983.555	4698248.467
2272-38951	7518958.517	4698256.320
2272-38876	7518959.738	4698282.408
2272-38875	7519004.768	4698285.976
2272-38879	7519020.438	4698286.115
2272-38891	7519017.407	4698265.946

Sip.graf.2211.9m²

Krijuar nga

Pozita:

Emri: Faton


Mbiemri: Bislimi

Emri i shfrytëzuesit(kodi): Faton.Bislimi

Data: 17.08.2020

Koha: 11:23:54

Nenshkrimi:

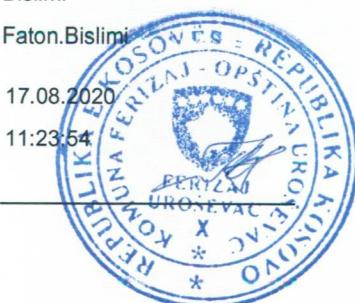




REPUBLIKA E KOSOVËS / REPUBLIKA KOSOVA / REPUBLIC OF KOSOVO
QEVERIA E KOSOVËS / VLADA KOSOVA / GOVERNMENT OF KOSOVA

MINISTRIA E EKONOMISË DHE AMBIENTIT / MINISTARSTVO EKONOMIJE I ŽIVOTNE SREDINE / MINISTRY OF ECONOMY AND ENVIRONMENT

AGJENCIA KADASTRALE E KOSOVËS / KATASTARSKA AGENCIJA KOSOVA / KOSOVA CADASTRAL AGENCY

Rapor i njësisë kadastrale

Zonë kadastrale: Rahovicë
Lloji i njësisë kadastrale: Parcelë
Nr i njësisë kadastrale: P-72217072-01712-1

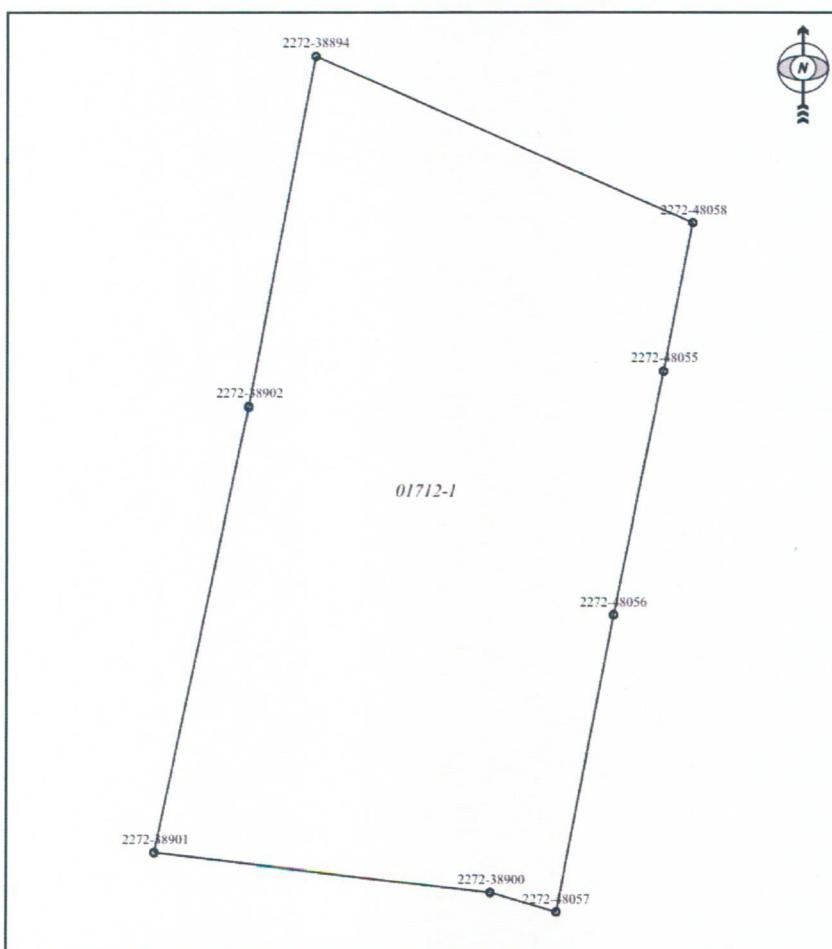

Pika	Y	X
2272-48058	7519071.732	4698184.635
2272-48055	7519068.220	4698166.790
2272-48056	7519062.230	4698137.550
2272-48057	7519055.380	4698101.950
2272-38900	7519047.431	4698104.283
2272-38901	7519006.881	4698108.894
2272-38902	7519018.253	4698162.481
2272-38894	7519026.305	4698204.809

Sip.graf.4376.7m²

Krijuar nga

Pozita:

Emri: Faton

Mbiemri: Bislimi

Emri i shfrytëzuesit(kodi): Faton.Bislimi

Data: 17.08.2020

Koha: 11:25:36

Nenshkrimi:





REPUBLIKA E KOSOVËS / REPUBLIKA KOSOVA / REPUBLIC OF KOSOVO

QEVERIA E KOSOVËS / VLADA KOSOVA / GOVERNMENT OF KOSOVA

MINISTRIA E EKONOMISË DHE AMBIENTIT / MINISTARSTVO EKONOMIJE I ŽIVOTNE SREDINE / MINISTRY OF ECONOMY AND ENVIRONMENT


AGJENCIA KADASTRALE E KOSOVËS / KATASTARSKA AGENCIJA KOSOVA / KOSOVA CADASTRAL AGENCY

Raport i njësisë kadastrale

Zonë kadastrale: Rahovicë

Lloji i njësisë kadastrale: Parcelë

Nr i njësisë kadastrale: P-72217072-01713-1

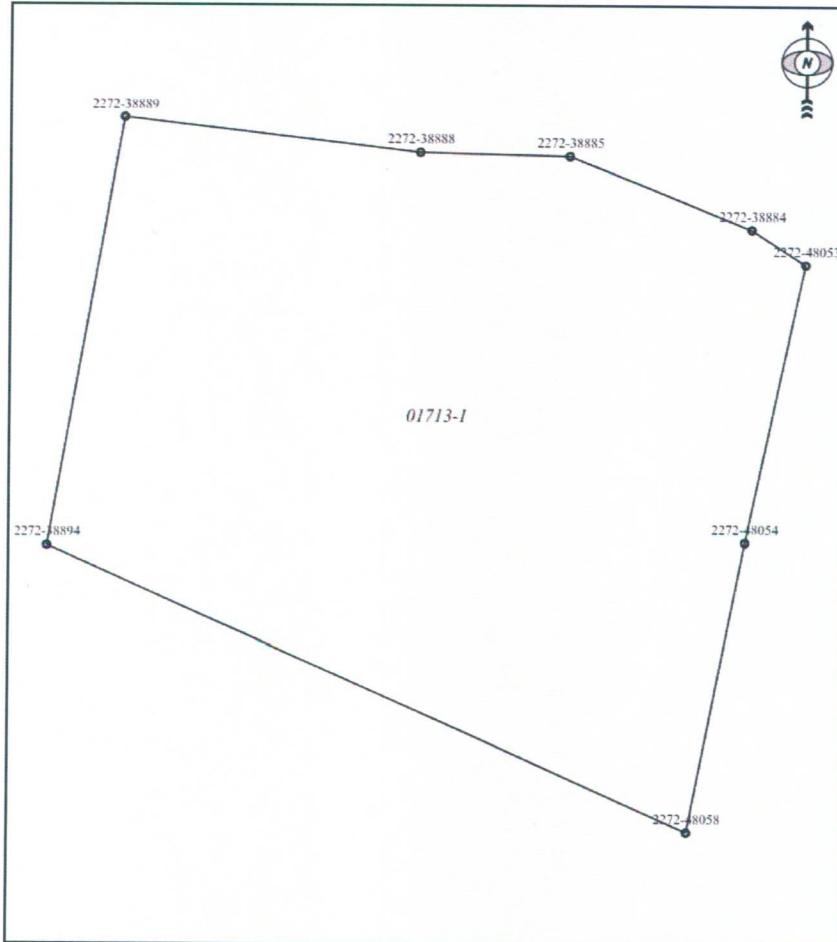

Pika	Y	X
2272-48053	7519079.990	4698224.900
2272-48054	7519075.770	4698205.150
2272-48058	7519071.732	4698184.635
2272-38894	7519026.305	4698204.809
2272-38889	7519031.706	4698235.117
2272-38888	7519052.676	4698232.686
2272-38885	7519063.256	4698232.446
2272-38884	7519076.146	4698227.376

Sip.graf.1846m²

Krijuar nga

Pozita:

Emri: Faton


Mbiemri: Bislimi

Emri i shfrytëzuesit(kodi): Faton.Bislimi

Data: 17.08.2020

Koha: 11:27:53

Nenshkrimi:

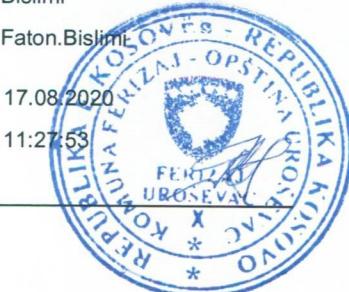



Numri i Protokollit

187/2020

Republika e Kosovës
Republika Kosova-Republic of Kosova
Qeveria -Vlada-Government

Ministria e Mjedisit dhe Planifikimit Hapësinor /Ministarstvo Sredine i Prostornog Planiranja/Ministry of Environment and Spatial Planning
AGJENCIA KADASTRALE E KOSOVËS/ KATASTARSKA AGECA KOSOVA/ KOSOVA CADASTRAL AGENCY

Formulari nr. 5

KËRKESË PËR SHERBIMET KADASTRALE NGA GJEODETI APO KOMPANIJA GJEODETE E LICENCUAR

Gjeodeti / Kompania gjeodete e licencuar: Liridon Sejdiu	Numri i licencës: 140
--	-----------------------

Komuna: Ferizaj	Zona Kadsatrale: Rahovicë
-----------------	---------------------------

Numri i njësisë kadastrale: 01949-1, 1713-1, 1712-2

1. Të dhënrat për parashtruesin e kërkesës

Emri / Emri i Kompanisë: Bedri	Mbiemri: Sylejmani	Emri i prindit: Mejdi
Numri personal: 1171039521	Adresa: Fsh. Rahovicë - Ferizaj	Nr. Tel: +383 44 378 904
Numri i biznesit: (për person juridik dhe kompani)		

2. Parashtruesi i kërkesës: Pronar - Shfrytëzues - Përfaqësues i Autorizuar

3. Lista e dokumenteve të nevojshme:

Pronari/Shfrytëzuesi	Përfaqësues i Autorizuar
1 <input checked="" type="checkbox"/> Letërnjoftimin / Certifikatë biznesi (kopje)	1 <input type="checkbox"/> Letërnjoftimin / Certifikatë biznesi (kopje)
2 <input checked="" type="checkbox"/> Vërtetimi i tatimit në pronë	2 <input type="checkbox"/> Vërtetimi i tatimit në pronë
3 <input type="checkbox"/> Çertifikata e pronës	3 <input type="checkbox"/> Çertifikata e pronës
4 <input type="checkbox"/> Kopja e planit	4 <input type="checkbox"/> Kopja e planit

4. Kërkesa për:

1 <input type="checkbox"/> Ndërrim të kulturës së parcelës	6 <input type="checkbox"/> Matjen dhe regjistrimin e ndërtësës
2 <input type="checkbox"/> Ndarjen e parcelës	7 <input type="checkbox"/> Matjen dhe regjistrimin e pjesës së ndërtësës
3 <input checked="" type="checkbox"/> Bashkimin e parcelës	8 <input type="checkbox"/> Punë të veçanta gjeodezike
4 <input type="checkbox"/> Përcaktimin e kufijve të parcelës	9 <input type="checkbox"/> Matja e ndërtësës për legalizim
5 <input type="checkbox"/> Ri-rregullimin e kufirit të parcelës	10 <input type="checkbox"/> Riregjistrim i pjesës grafike

Nënshkrimi: Bajrami
Data: 13.08.2020



REPUBLIKA E KOSOVËS - REPUBLIKA KOSOVA - REPUBLIC OF KOSOVA
KOMUNA FERIZAJ - OPŠTINA UROŠEVAC - MUNICIPALITY OF FERIZAJ



Formulari per kerkese apo ankesë

Drejtoriati/Njesia

Drejtoria e Pronës, Kadastrit dhe Gjeodezisë

Data 14/08/2020

1. Informatat personale te parashtruesit te kerkesës:

Emri dhe mbiemri

Liridon Sejdiu

Adresa e vendbanimit

Greme

Numri i tel. fiks

Numri i tel. mobil

044-489-498

Numri personal

1174982178

E-mail Adresa

Vlera për pagesë: 40.00

2. Mënyra e pranimit

Statusi i lëndës

Kërkesa

Ne proces

Mos shkruani në këtë pjesë

Numri i protokolit

10-942/05-0063788/20

Afati i zgjedhjes

13/09/2020

Vendimi

3. Ju lutemi të shkruani kërkesën apo ankesën tuaj në detaje:

Kërkesë për blerje të produkteve kadastrale

1712-1, 1714-0, 1946-0, 1950-1

1713-1, 1715-0, 1949-1, RAHOVICË

4. Dokumentet e bashkangjitura:

Nr. Lloji i dokumentit

5. Dëshmia e aplikuesit për vërtetësi

Unë Liridon Sejdiu vërtetoj se informatat e lartshënuara janë të vërteta.

(Nënshkrimi)

*Ju lutemi të kérkonai nga zyrtari/ja fletëdëshminë për dorëzimin e kësaj kërkeze dhe dokumenteve të bashkangjitura

Pranuar nga: Shpresa.Topalli



Data: 14.08.2020 13:44:21

DEBI:	40.00
KREDI:	41.00
PROVIZIONI:	1.00

LLOGARIA: KOMUNA FERIZAJ
NUMRI I LLOGARISE: 1000650030000035
REFERENCA: FEG9D25200018339
PAGOI: LIRIDON SEJDIU
NR.SERIK: 2520001833
PERSHKRIMI: 10-942/05-0063788/20
PER: KERKSE PER BLERJEN E PRODUKTEVE KADASTRALE

Shendrit Shabani B.I
sh.shabani

Pagoi:





Matje Gjeodezike
Shërbime Kadastrale
Projektime Inxhinierike
Tel: +383 (0) 49-535-250
liridonsejdiu88@gmail.com

N.SH. "Geo Coding"

Faturë

Nr: 24/2020

Shitësi:

N.SH. "Goe Coding"

Pronari:	LIRIDON SEJDIU
NRB:	811384528
Numri Fiskal:	811384528
Adresa:	Rr. "12 Qershori" - Ferizaj
BPB - 13-04-0010027832.69	
LL/Bankare	130400100278326000.00%

Blerësi:

Bedri (Mejdi) Sylejmani

Nr. ID.	1171039521
NRB:	
Nr. Fiskal:	
Adresa:	
LL/Bankare	

Nr.	Përshkrimi	Njësi matëse	Sasia	Çmimi	Vlera totale
1	Ndarje e parcelës kadastrale nr 01949-1,02310-0 Z.K. Rahovicë	cop	6	20.00	120.00
					-
					-
					-
					-
					-
Totali:					€ 120.00

Data: 27.08.2020

Pagesa: Cash

Komenti: 1. BPB 13-04-0010027832.69
2. Banka Ekonomike 1304001002783269

Pranoi:

Dorëzoi:





Republika e Kosovës

Republika Kosova - Republic of Kosovo

Qeveria e Kosovës - Vlada Kosova - Government of Kosovo

Ministria e Infrastrukturës dhe Ambientit/ Ministrastvo Infrastrukture i Sredine/ Ministry of Infrastructure and Environment

AGJENCIA KADASTRALE E KOSOVËS/ KOSOVSKA KATASTARSKA AGENCIJA/ KOSOVA CADASTRAL AGENCY

MBËSHTJELLËS I LËNDËS

Gjeodeti / Kompania gjeodete e licencuar: **LIRIDON SEJDIU**

Numri i licencës: **140**

Numri i Protokollit: **187/2020**

LËNDA:

1. Ndërrim të kulturës së parcelës
2. Ndarjen e parcelës
3. Bashkimin e parcelës
4. Përcaktimin e kufijve të parcelës
5. Ri-rregullimin e kufirit të parcelës
6. Matjen dhe regjistrimin e ndërtesës
7. Matjen dhe regjistrimin e pjesës së ndërtesës
8. Regjistrimi i servitutit
9. Punë të veçanta gjeodezike
10. Matja e ndërtesës për legalizim

“GJEODET I LICENCUAR”

+383 49 535 250

e-mail: liridonsejdiu88@gmail.com

Data: **27/08/2020**

Vendi: **FERIZAJ**

.....

(Nënshkrimi dhe vula)

Përbajtja:

1. Kërkesa e palës
 2. Dëshmia e burimit të të dhënave zyrtare
 3. Dëshmia e pagesës për të dhënat e pranuara
 4. Fatura apo kuponii fiskal e lëshuar shërbimet kadastrale sipas UA 11/2019 dhe 12/2019
 5. Procesverbali nga terreni
 6. Manuali i njësive kadastrale
 7. Regjistri i ndërrimeve
 8. Lista e koordinatave të matura
 9. Formulari i korrigjimit të sipërfaqes
 10. Letërnjoftimi i pronarit
 11. Certifikatën e pronësisë
 12. Raporti teknik
 13. Letërnjoftimi kopje i fqinjëve
 14. Dokumentacioni i gjeodetit të licencuar

Dokumente tjera:



Дата е ёштим / Датум издавања / Date of issue

31.12.2018

Лештар пог / Издат од / Issued by

МРВ / МУР / МИА

№. Personal / Лични Бр. / Personal No.

1171039521

№. Lнг / Бр. Л.К. / ID Card No.

ID1156577

Вендалими / Пребивалиште / Residence

FERIZAJ

I DRKSID11565777<<<<<<<<<<<
5705159M2812302RKS1171039521<6
STYLEJMANI<<BEDRI<<<<<<<<<



Republika e Kosovës / Republika Kosova / Republic of
Komuna e FERIZAJ / Opština UROŠEVAC / Municipality



Bazuar në nenin 18 të ligjit 03/L-204 për tatimin në pronë, si dhe udhëzimit administrativ nr. 7/2011 të lëshuar nga MF, i cili ka të bëjë me urdhëresat e ndalimit të shërbimeve komunale për detyrim të pagesës së tatimit në

Na osnovu člana 18, zakona 03/L-204 za poreza na imovinu i administrativne uredbe MF br. 7/2011, u vezi zabrane opštinske usluga za prinudu uplate poreza na imovinu, izdaje se ova:

Based on the article 18 of LAW 03/L-204 on property tax and administrative instruction MF no. 7/2011 on termination of services for enforcement of the municipal property tax, the municipal Property Tax Office

Nr / Br / No

22527465

20/07/2020

VËRTETIM POTVRDA CERTIFICATE

Me të cilin vërtetohet se tatimpaguesi
Kojim se potvrđuje da je poreznik
that certifies that taxpayer

BEDRI SYLEJMANI

FERIZAJ

Komuna / Opština / Municipality

FERIZAJ ESAD MEKULI

adresa / address

I ka kryer pjesërisht / plotësisht obligimet e tatimit në pronë
Delimično/ izveršio uplatu poreskih obaveza
has partially / fulfilled obligations on property tax

BEDRI SYLEJMANI

Vërtetimi lëshohet në bazë të kërkesës së / Potvrda se izdaje na zahev / Certificate is issued by

Për nevoja personale

dhe shërben për / i služi za / and is used for

Shënimë shësë / Druge podatke / Aditonal info



Nenshkrimi / Potpis / Signature

Numrat kadastrale 1946	Numri i certifikatës IPRR	Komuna: Ferizaj
Zloji i njësisë kadastrale Zgjedh	Zona Kadastrale RAHOVICE	
Pronari ...	Kërko	
Lloji i së drejtës		

Shiko 10 rreshta	Kërko:						
Aktiv	Numri kadastrale	Numri i certifikatës në RDPP	Komuna	Zona Kadastrale	Adresa	Lloji i njësisë kadastrale	Sipërfaqja
Zgjedh Aktiv	P-72217072-01946-0	330	Ferizaj	RAHOVICE	XHELPSINE	PARCELE	1723 m ²
Duke treguar 1 deri 1 prej 1 rreshtave.							
						E Kaluara.	1 Tjetra.
Numri kadastrale		P-72217072-01946-0					
Numri elektronik kadastrale		452896					
Lloji i njësisë kadastrale		Parcelë					
Sipërfaqja		1723					
Përshkrimi		2-RDPP-Kontrate mbi faljen VR.nr.2438/2003; dt.10.03.2003 Gj.K.Ferizaj					
Numri i listës së njësive		UL-72217072-00330					
Numri i Certifikatave		330					
Lloji i rrugës							
Emri i rrugës							
Përshkrimi i adresës		XHELPSINE					
Fillimi i vlefshmëris se lëndës		Migrimi Ferizaj / 20.09.2012					
Azhurnimi i Fundit i Lëndës							
Aktiv							
Shiko 10 rreshta	Kërko:						
Komponenti i të drejtave	Emri i Personit	Kushtet dhe afatet		Përshkrimi			
Posedim							
Posedim individual	SYLEJMANI HALIL						
Duke treguar 1 deri 2 prej 2 rreshtave.							

Numrat kadastrale 1949	Numri i certifikatës IPRR	Komuna: Ferizaj
Zgjedh		Zona Kadastrale RAHOVICEË
Lloji i njësisë kadastrale		
Zgjedh	...	Kërko
Pronari		
Lloji i së drejtës		
X		

Shiko 10 rreshta								Kërko:
Aktiv	Numri kadastrale	Numri i certifikatës në RDPP	Komuna	Zona Kadastrale	Adresa	Lloji i njësisë kadastrale	Sipërfaqja	
Zgjedh	Aktiv P-72217072-01949-1	4	Ferizaj	RAHOVICEË	XHELPSINA	PARCELË	2212 m2	
Zgjedh	Aktiv P-72217072-01949-2	4	Ferizaj	RAHOVICEË	XHELPSINA	PARCELË	51 m2	

Duke treguar 1 deri 2 prej 2 reshtave.

Numri kadastrale	P-72217072-01949-1
Numri elektronik kadastrale	2253973
Lloji i njësisë kadastrale	Parcelë
Sipërfaqja	2212
Përshkrimi	20/2016, RFP.5/2016
Numri i listës së njësive	UL-72217072-00004
Numri i Certifikatave	4
Lloji i rrugës	
Emri i rrugës	
Përshkrimi i adresës	XHELPSINA
Fillimi i vlefshmëris se lëndës	58454/2016 / 14.06.2016
Azhurnimi i Fundit i Lëndës	58454/2016 / 14.06.2016
Aktiv	Aktiv

Shiko 10 rreshta

Kërko:

Komponenti i të drejtave	Emri i Personit	Kushtet dhe afatet	Përshkrimi
Posedim 9500 EUR			
Posedim individual	SYLEJMANI BEDRI	Kontratë mbi shitblerjen e paluajteshmerisë LRP.nr.3642/2014, Nr.ref.1244/2014	23/2014

Duke treguar 1 deri 2 prej 2 reshtave.

Numrat Kadastrale	Numri i certifikatës IPRR	Komuna: Ferizaj
1950		Zona Kadastrale RAHOVICE
Lloji i njësisë kadastrale		
Zgjedh		
Pronari		
	...	Kërko
Lloji i së drejtës		

Shiko 10 rreshta								Kërko:
Aktiv	Numri kadastrale	Numri i certifikatës në RDPP	Komuna	Zona Kadastrale	Adresa	Lloji i njësisë kadastrale	Sipërfaqja	
Zgjedh	Aktiv P-72217072-01950-1	128	Ferizaj	RAHOVICE	XHELPSINE	PARCELE	3680 m2	
Zgjedh	Aktiv P-72217072-01950-2	128	Ferizaj	RAHOVICE	XHELPSINE	PARCELE	225 m2	

Duke treguar 1 deri 2 prej 2 rreshtave.

E Kaluara. 1 Tjetra.

Numri kadastrale	P-72217072-01950-1
Numri elektronik kadastrale	452901
Lloji i njësisë kadastrale	Parcelë
Sipërfaqja	3680
Përshkrimi	
Numri i listës së njësive	UL-72217072-00128
Numri i Certifikatave	128
Lloji i rrugës	
Emri i rrugës	
Përshkrimi i adresës	XHELPSINE
Fillimi i vlefshmëris se lëndës	Migrimi Ferizaj / 20.09.2012
Azhurnimi i Fundit i Lëndës	
Aktiv	Aktiv

Komponenti i të drejtave	Emri i Personit	Kushtet dhe afatet	Përshkrimi
Posedim			
Posedim individual	STYLEJMANI MEJDI		

Duke treguar 1 deri 2 prej 2 rreshtave.

E Kaluara. 1 Tjetra.

Numrat kadastrale 1714	Numri i certifikatës IPRR	Komuna: Ferizaj
Zloji i njësisë kadastrale Zgjedh		Zona Kadastrale RAHOVICE
Pronari ...	<input type="button" value="Kërko"/>	
Lloji i së drejtës		
<input type="text"/> <input type="button" value="X"/>		

Shiko 10 rreshta								Kërko:
Aktiv	Numri kadastrale	Numri i certifikatës në RDPP	Komuna	Zona Kadastrale	Adresa	Lloji i njësisë kadastrale	Sipërfaqja	
Zgjedh	Aktiv P-72217072-01714-0	49	Ferizaj	RAHOVICE	XHELPSINE	PARCELË	772 m ²	

Duke treguar 1 deri 1 prej 1 rreshtave.

<input type="button" value="E Kaluara."/>	<input type="button" value="1"/>	<input type="button" value="Tjetra."/>
---	----------------------------------	--

Numri kadastrale	P-72217072-01714-0
Numri elektronik kadastrale	452653
Lloji i njësisë kadastrale	Parcelë
Sipërfaqja	772
Përshkrimi	
Numri i listës së njësive	UL-72217072-00049
Numri i Certifikatave	49
Lloji i rrugës	
Emri i rrugës	
Përshkrimi i adresës	XHELPSINE
Fillimi i vlefshmëris se lëndës	Migrimi Ferizaj / 20.09.2012
Azhurnimi i Fundit i Lëndës	
Aktiv	Aktiv

Shiko 10 rreshta		Kërko:	
Komponenti i të drejtave	Emri i Personit	Kushtet dhe afatet	Përshkrimi
Posedim			
Posedim individual	MUSLIU HANUMSHAHE		

Duke treguar 1 deri 2 prej 2 rreshtave.

<input type="button" value="E Kaluara."/>	<input type="button" value="1"/>	<input type="button" value="Tjetra."/>
---	----------------------------------	--

Numrat kadastrale 1715	Numri i certifikatës IPRR	Komuna: Ferizaj
Zloji i njësisë kadastrale Zgjedh		Zona Kadastrale RAHOVICE
Pronari ...	<input type="button" value="Kërko"/>	
Lloji i së drejtës <input type="text"/>		

Shiko 10 ▼ rreshta	Kërko: <input type="text"/>						
Aktiv	Numri kadastrale	Numri i certifikatës në RDPP	Komuna	Zona Kadastrale	Adresa	Lloji i njësisë kadastrale	Sipërfaqja
Zgjedh Aktiv	P-72217072-01715-0	49	Ferizaj	RAHOVICË	XHELPSINE	PARCELË	2798 m ²

Duke treguar 1 deri 1 prej 1 rreshtave.

E Kaluara.	1	Tjetra.
------------	---	---------

Numri kadastrale	P-72217072-01715-0
Numri elektronik kadastrale	452654
Lloji i njësisë kadastrale	Parcelë
Sipërfaqja	2798
Përshkrimi	
Numri i listës së njësive	UL-72217072-00049
Numri i Certifikatave	49
Lloji i rrugës	
Emri i rrugës	
Përshkrimi i adresës	XHELPSINE
Fillimi i vlefshmëris se lëndës	Migrimi Ferizaj / 20.09.2012
Azhurnimi i Fundit i Lëndës	
Aktiv	Aktiv

Shiko 10 ▼ rreshta

Kërko:

Komponenti i të drejtave	Emri i Personit	Kushtet dhe afatet	Përshkrimi
Posedim			
Posedim individual	MUSLIU HANUMSHAHE		

Duke treguar 1 deri 2 prej 2 rreshtave.

E Kaluara.	1	Tjetra.
------------	---	---------

Numrat kadastrale 1713	Numri i certifikatës IPRR	Komuna: Ferizaj
Zloji i njësisë kadastrale Zgjedh		Zona Kadastrale RAHOVICE
Pronari ...	<input type="button" value="Kërko"/>	
Lloji i së drejtës <input type="text"/>		

Shiko 10 rreshta Kërko:

Aktiv	Numri kadastrale	Numri i certifikatës në RDPP	Komuna	Zona Kadastrale	Adresa	Lloji i njësisë kadastrale	Sipërfaqja
Zgjedh	Aktiv P-72217072-01713-1	48	Ferizaj	RAHOVICE	XHELPSINA	PARCELË	1878 m2
Zgjedh	Aktiv P-72217072-01713-2	48	Ferizaj	RAHOVICE	XHELPSINA	PARCELË	364 m2

Duke treguar 1 deri 2 prej 2 rreshtave.

Numri kadastrale	P-72217072-01713-1
Numri elektronik kadastrale	452651
Lloji i njësisë kadastrale	Parcelë
Sipërfaqja	1878
Përshkrimi	Coptimi eshte bere me kerkesen e pales 971/09; dt.29.07.2009; pala ka percaktuar me pare kufijt eparceles
Numri i listës së njësive	UL-72217072-00048
Numri i Certifikatave	48
Lloji i rrugës	
Emri i rrugës	
Përshkrimi i adresës	XHELPSINA
Fillimi i vlefshmëris se lëndës	Migrimi Ferizaj / 20.09.2012
Azhurnimi i Fundit i Lëndës	
Aktiv	Aktiv

Shiko 10 rreshta Kërko:

Komponenti i të drejtave	Emri i Personit	Kushtet dhe afatet	Përshkrimi
Posedim 9000 EUR 31.07.2018			
Posedim individual	SYLEJMANI BEDRI	Kontratë për shitblerjën e paluajtshmërisë LRP.nr.3820/2018, Nr.ref.1061/2018	19/2018

Duke treguar 1 deri 2 prej 2 rreshtave.



Republika e Kosovës
Republika Kosova-Republic of Kosovo
Qeveria e Kosovës- Vlada Kosova- Government of Kosovo
Ministria e Infrastrukturës dhe Ambientit/ Ministrastvo Infrastrukture i Sredine/ Ministry of Infrastructure and Environment

AGJENCIA KADASTRALE E KOSOVËS/KOSOVSKA KATASTARSKA AGENCIJA/ KOSOVO CADASTRAL AGENCY

PROCESVERBALI NGA TERRENI

Gjeodeti / Kompania gjeodete e licencuar: Liridon Sejdiu	Numri i licencës: 140
--	-----------------------

Komuna: Ferizaj	Zona Kadastrale: RAHOVICE
-----------------	---------------------------

Numri i njësisë kadastrale: 01849-1, 1712-1, 1713-1

Matja/piketimi është realizuar me:
GPS/GNSS <input checked="" type="checkbox"/>
Stacion Total <input type="checkbox"/>

1. Përshkimi i procesit:

*NDARJA E PARCE. 1849-1 BEFAET SI PAS GJENDJES FAKTIKE.
PARCELAT 1712-1 DHE 1713-1 (ME PIESË E TËRSIJE SE ARAVSINDATEK
ME SIP. TË BARABARTA, PËRPOS NJERËZ HISE QË KA SËBIRË NË SHUMË.*

2. Vërejtje:

*PALET JANE MJOFTUAR PËR SHPËRPUTHJEN MËSS SIP. NË REGJISTRIM
SIKTOK DHE GJENDJES FAKTIKE.*

3. Nënshkrimi i palëve

Pronarët janë pajtuar me pikat definitive kufitare të vendosura në terren nga të cilat derivohet sipërfaqja definitive që do të regjistrohet në Sistemin e Informacioneve Kadastrale për Tokën në Kosovë.

Të poshtëshënuarve u lexohet procesverbal dhe nëse pajtohen me atë nënshkruajnë më poshtë, në të kundërtën jepin arsyet e mospajtimit.

Emri (emri i prindit) mbiemri	Numri personal	Numri i njësisë kadastrale	Nënshkrimi
BEDRI SULEJMANI	1171039521	1849-1, 1712-1, 1713-1	<i>Bedri Sulejmani</i>
GASHIRE SULEJMANI	1005081803		<i>Gashire Sulejmani</i>
SALIH SULEJMANI	100093819		<i>Salih Sulejmani</i>

Nënshkrimi dhe vula e gjodetit: *RJ*

Data: 15.08.2020



Republika e Kosovës
Republika Kosova-Republic of Kosova
Qeveria - Vlada-Government
Ministria e Mjedisit dhe Planifikimit Hapësinor /Ministarstvo Sredine i Prostornog Planiranja/Ministry of Environment and Spatial Planning
AGJENCIJA KADASTRALE E KOSOVËS/ KATASTARSKA AGECIJA KOSOVA/ KOSOVA CADASTRAL AGENCY

Zyra kadastrale komunale / Opštinska katastarska kancelarija: Ferizaj


Nr. i njësisë kadastrale / Br. katastarske jedinice : 1949-1,2310-0

Zona kadastrale / Katastarska zona: Rahovicë

Numri i lëndës / Broj predmeta: _____

Lloji i njësisë kadastrale / Vrsta katastarske jedinice : Parcel

Shkalla e zvoglimit / Razmerra plana : 1:1000

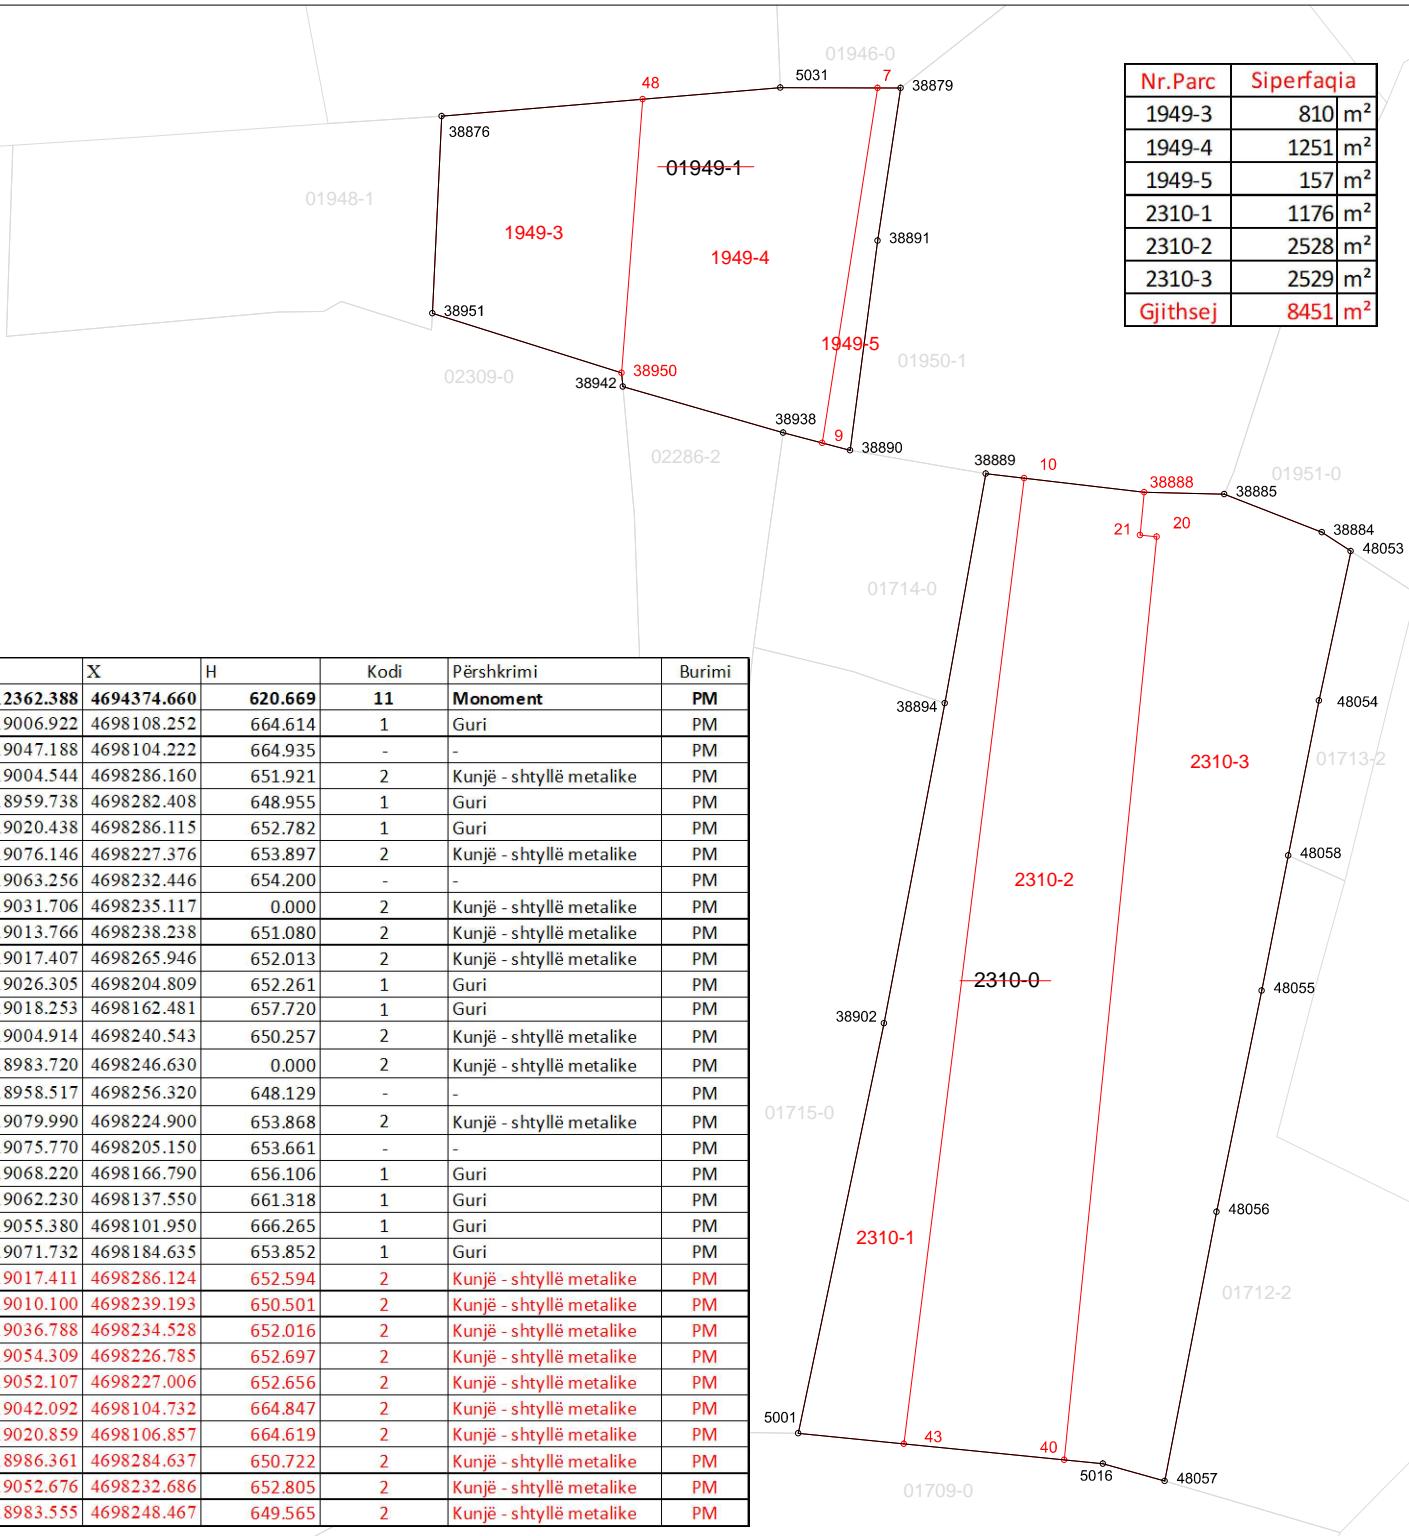

Nr	Y	X	H	Kodi	Përshkrimi	Burimi
220086	7512362.388	4694374.660	620.669	11	Monoment	PM
5001	7519006.922	4698108.252	664.614	1	Guri	PM
5016	7519047.188	4698104.222	664.935	-	-	PM
5031	7519004.544	4698286.160	651.921	2	Kunjë - shtyllë metalike	PM
38876	7518959.738	4698282.408	648.955	1	Guri	PM
38879	7519020.438	4698286.115	652.782	1	Guri	PM
38884	7519076.146	4698227.376	653.897	2	Kunjë - shtyllë metalike	PM
38885	7519063.256	4698232.446	654.200	-	-	PM
38889	7519031.706	4698235.117	0.000	2	Kunjë - shtyllë metalike	PM
38890	7519013.766	4698238.238	651.080	2	Kunjë - shtyllë metalike	PM
38891	7519017.407	4698265.946	652.013	2	Kunjë - shtyllë metalike	PM
38894	7519026.305	4698204.809	652.261	1	Guri	PM
38902	7519018.253	4698162.481	657.720	1	Guri	PM
38938	7519004.914	4698240.543	650.257	2	Kunjë - shtyllë metalike	PM
38942	7518983.720	4698246.630	0.000	2	Kunjë - shtyllë metalike	PM
38951	7518958.517	4698256.320	648.129	-	-	PM
48053	7519079.990	4698224.900	653.868	2	Kunjë - shtyllë metalike	PM
48054	7519075.770	4698205.150	653.661	-	-	PM
48055	7519068.220	4698166.790	656.106	1	Guri	PM
48056	7519062.230	4698137.550	661.318	1	Guri	PM
48057	7519055.380	4698101.950	666.265	1	Guri	PM
48058	7519071.732	4698184.635	653.852	1	Guri	PM
7	7519017.411	4698286.124	652.594	2	Kunjë - shtyllë metalike	PM
9	7519010.100	4698239.193	650.501	2	Kunjë - shtyllë metalike	PM
10	7519036.788	4698234.528	652.016	2	Kunjë - shtyllë metalike	PM
20	7519054.309	4698226.785	652.697	2	Kunjë - shtyllë metalike	PM
21	7519052.107	4698227.006	652.656	2	Kunjë - shtyllë metalike	PM
40	7519042.092	4698104.732	664.847	2	Kunjë - shtyllë metalike	PM
43	7519020.859	4698106.857	664.619	2	Kunjë - shtyllë metalike	PM
48	7518986.361	4698284.637	650.722	2	Kunjë - shtyllë metalike	PM
38888	7519052.676	4698232.686	652.805	2	Kunjë - shtyllë metalike	PM
38950	7518983.555	4698248.467	649.565	2	Kunjë - shtyllë metalike	PM

Rilevoi / Snimio: LIRIDON SEJDIU
 (emri dhe mbiemri i gjeodetit/kompanisë/ ime i prezime geodeta/ kompanije)

Nr. i licencës / Br. licence: 140

V.V.

Nënshkrimi / Potpis:

Data e rilevimit / Datum snimanja: 15.08.2020

Aprovoi / Usvojio: _____
 (emri dhe mbiemri i pësonit zyrtar/ ime i prezime sluzbenog lica)

Nënshkrimi / Potpis:

Data e aprovimit / Datum usvajanja: _____

Open Documents								
	Point Id	Point Class	Date/Time	Easting	Northing	Ellip. Hgt.	Code	Posn. + Hgt. Qlty
2310-0-Rahovice	✓ 100	Measured	08/15/2020 10:09:25	7519062.5269	4698303.7439	655.4843	MURI	0.0331
	✓ 101	Measured	08/15/2020 10:09:55	7519068.9257	4698303.7654	655.8211	MURI	0.0273
	✓ 102	Measured	08/15/2020 10:11:29	7519041.3085	4698303.5844	654.1120	GURI	0.0466
	✓ 103	Measured	08/15/2020 10:14:19	7519009.1813	4698286.2231	652.1635	RRETHOJ	0.0298
	✓ 105	Measured	08/15/2020 10:19:53	7518985.6539	4698284.3726	650.5529	GURI	0.0969
	✓ 106	Measured	08/15/2020 10:20:28	7518985.6506	4698284.3778	650.7224	GURI	0.0400
	✓ 107	Measured	08/15/2020 10:21:26	7518986.3685	4698284.7403	650.6527	RRETHOJ	0.0669
	✓ 108	Measured	08/15/2020 10:21:39	7518986.3693	4698284.7380	650.7477	RRETHOJ	0.0373
	✓ 109	Measured	08/15/2020 10:22:39	7518985.2633	4698266.7560	650.2268	GURI	0.0266
	✓ 111	Measured	08/15/2020 11:52:38	7519043.4185	4698329.9105	653.4877	ARMATUR	0.0305
	✓ 112	Measured	08/15/2020 11:53:03	7519043.0150	4698330.7161	653.5431	ARMATUR	0.0251
	✓ A1	Measured	08/15/2020 13:47:19	7519072.3798	4698299.7688	656.0519		0.0267
	✓ A2	Measured	08/15/2020 14:05:58	7519054.8282	4698296.6968	654.7625		0.0202
	✓ A3	Measured	08/15/2020 14:12:16	7519036.8059	4698296.5972	653.8523		0.0307
	✓ A5	Measured	08/15/2020 14:10:15	7519041.3373	4698303.6429	654.1288		0.0441
	✓ A6	Measured	08/15/2020 14:17:11	7519009.0506	4698286.1409	652.2577		0.0271
	✓ A7	Measured	08/15/2020 14:15:52	7519017.4409	4698286.1393	652.5935		0.0254
	✓ A9	Measured	08/15/2020 14:22:43	7519010.1292	4698239.1077	650.5014		0.0893
	✓ A10	Measured	08/15/2020 14:28:22	7519036.8342	4698234.5322	652.0161		0.0462
	✓ A11	Measured	08/15/2020 14:34:43	7519056.9291	4698232.6006	653.1490		0.0210
	✓ A12	Measured	08/15/2020 15:32:45	7519036.9022	4698104.9648	665.0357		0.0483
	✓ A14	Measured	08/15/2020 15:45:11	7518998.5864	4698108.4058	663.5423		0.0273
	✓ A15	Measured	08/15/2020 13:50:11	7519062.5633	4698299.7646	655.3970		0.0202
	✓ A16	Measured	08/15/2020 13:52:09	7519063.3933	4698303.7651	655.9778		0.0398
	✓ A18	Measured	08/15/2020 14:01:35	7519055.5221	4698314.9715	654.8515	GURI	0.0185
	✓ A20	Measured	08/15/2020 15:07:01	7519054.3005	4698226.7895	652.6967		0.0191
	✓ A21	Measured	08/15/2020 15:08:31	7519052.0144	4698227.0085	652.6562		0.0211
	✓ A22	Measured	08/15/2020 16:04:14	7519058.9722	4698299.7124	655.1131		0.0429
	✓ A40	Measured	08/24/2020 16:16:59	7519042.1023	4698104.7793	664.8470		0.0378
	✓ A41	Measured	08/24/2020 15:50:30	7519073.1805	4698298.7669	656.1590		0.0247
	✓ A42	Measured	08/24/2020 16:58:23	7519058.4081	4698293.6989	655.1378		0.0423
	✓ A43	Measured	08/24/2020 16:59:37	7519065.6520	4698295.0331	655.4771		0.0273
	✓ A48	Measured	08/24/2020 16:25:39	7518986.3767	4698284.6314	650.7218		0.0216
	✓ A200	Measured	08/15/2020 14:59:16	7519063.6630	4698231.7411	653.7386	GURI	0.0295
	✓ A300	Measured	08/15/2020 16:19:24	7519081.6461	4698287.4977	658.4002		0.0441
	✓ A301	Measured	08/15/2020 16:21:34	7519085.9124	4698285.9076	657.5732		0.0247
	✓ A5001	Measured	08/15/2020 11:15:10	7519006.8743	4698108.8972	664.3022		0.0569
	✓ A5002	Measured	08/15/2020 15:48:44	7518988.8543	4698108.5628	663.7282		0.0235
	✓ A5003	Measured	08/15/2020 11:08:47	7518981.1876	4698109.1636	664.1450		0.0577
	✓ A5004	Measured	08/15/2020 11:02:08	7518984.6071	4698136.4261	661.5310		0.0260
	✓ A5005	Measured	08/15/2020 10:59:37	7518988.8578	4698160.5436	658.3380		0.0476
	✓ A5006	Measured	08/15/2020 10:58:31	7518996.5890	4698161.5753	657.9794		0.0350
	✓ A5007	Measured	08/15/2020 10:56:33	7518998.1477	4698185.2690	653.6043		0.0423
	✓ A5008	Measured	08/15/2020 10:50:01	7519000.9771	4698212.1695	651.2296		0.0228
	✓ A5010	Measured	08/15/2020 10:51:19	7519026.3057	4698204.8171	652.2612		0.0245
	✓ A5011	Measured	08/15/2020 10:53:06	7519018.2796	4698162.4775	657.6428		0.0258
	✓ A5012	Measured	08/15/2020 15:26:39	7519071.6454	4698184.6343	653.8521		0.0286
	✓ A5013	Measured	08/15/2020 15:27:32	7519068.1797	4698166.7916	656.1059		0.0262
	✓ A5014	Measured	08/15/2020 15:28:32	7519062.2286	4698137.5278	661.3178		0.0229
	✓ A5015	Measured	08/15/2020 15:30:13	7519055.3962	4698102.0171	666.2647		0.0323
	✓ A5016	Measured	08/15/2020 11:19:12	7519047.1877	4698104.2225	664.9353	GURI	0.0337
	✓ A5017	Measured	08/15/2020 14:52:42	7519063.2143	4698232.4549	654.2004		0.0414

Open Documents		Point Id	/	Point Class	Date/Time	Easting	Northing	Ellip. Hgt.	Code	Posn. + Hgt. Qty
		A5008		Measured	08/15/2020 10:50:01	7519000.9771	4698212.1695	651.2296		0.0228
		A5010		Measured	08/15/2020 10:51:19	7519026.3057	4698204.8171	652.2612		0.0245
		A5011		Measured	08/15/2020 10:53:06	7519018.2796	4698162.4775	657.6428		0.0258
		A5012		Measured	08/15/2020 15:26:39	7519071.6454	4698184.6343	653.8521		0.0286
		A5013		Measured	08/15/2020 15:27:32	7519068.1797	4698166.7916	656.1059		0.0262
		A5014		Measured	08/15/2020 15:28:32	7519062.2286	4698137.5278	661.3178		0.0229
		A5015		Measured	08/15/2020 15:30:13	7519055.3962	4698102.0171	666.2647		0.0323
		A5016		Measured	08/15/2020 11:19:12	7519047.1877	4698104.2225	664.9353	GURI	0.0337
		A5017		Measured	08/15/2020 14:52:42	7519063.2143	4698232.4549	654.2004		0.0414
		A5018		Measured	08/15/2020 15:01:12	7519076.0881	4698227.4687	653.8973	GURI	0.0245
		A5019		Measured	08/15/2020 15:03:08	7519079.9795	4698224.9140	653.8680	GURI	0.0458
		A5020		Measured	08/15/2020 15:13:06	7519075.7498	4698205.1200	653.6608		0.0292
		A5021		Measured	08/15/2020 15:14:27	7519072.1628	4698187.3182	654.0730		0.0222
		A5023		Measured	08/15/2020 14:32:46	7519052.6786	4698232.7134	652.8054		0.0562
		A5024		Measured	08/15/2020 10:48:31	7519003.0038	4698227.0572	650.4440		0.0161
		A5025		Measured	08/15/2020 10:42:46	7519004.9118	4698240.5364	650.2568		0.0312
		A5026		Measured	08/15/2020 10:40:13	7519013.7829	4698238.2402	651.0798		0.0430
		A5028		Measured	08/24/2020 16:40:12	7518984.0768	4698248.4075	649.5650		0.0319
		A5029		Measured	08/24/2020 16:35:51	7518958.5572	4698256.2144	648.1294		0.0491
		A5030		Measured	08/24/2020 16:27:07	7518959.7540	4698282.4154	648.9548		0.0111
		A5031		Averaged	08/15/2020 16:15:29	7519004.5407	4698286.1472	651.9206	GURI	0.0210
		A5032		Measured	08/15/2020 10:37:02	7519020.4489	4698286.1301	652.7573		0.0335
		A5033		Measured	08/15/2020 10:37:51	7519017.3856	4698265.9425	652.0129		0.0239
		A5036		Measured	08/15/2020 14:54:26	7519064.5087	4698235.2808	654.1974		0.0204
		A5037		Measured	08/15/2020 10:35:03	7519041.6330	4698302.8643	653.9789		0.0299
		A5038		Measured	08/15/2020 10:05:23	7519064.0699	4698302.8424	655.4474		0.0231
		A5039		Measured	08/15/2020 10:03:42	7519069.8200	4698303.0534	655.8573		0.0209
		A5040		Measured	08/15/2020 11:58:10	7519004.7684	4698325.1260	652.0476		0.0424
		A220086		Measured	08/24/2020 19:15:35	7512362.3880	4694374.6600	620.6690		0.0254
		AA16		Measured	08/15/2020 13:58:13	7519062.5419	4698303.7444	655.5176		0.0394
		AA5001		Measured	08/15/2020 11:16:00	7519006.9220	4698108.2515	664.6144	GURI	0.0417
		AA5003		Measured	08/15/2020 11:10:03	7518981.1712	4698109.1553	663.7885		0.0392
		B5001		Measured	08/15/2020 15:52:40	7519006.9560	4698108.2656	664.5990		0.0191
		B5010		Measured	08/15/2020 15:59:39	7519026.3200	4698204.7926	652.4578		0.0145
		B5011		Measured	08/15/2020 15:56:52	7519018.2665	4698162.4968	657.7201		0.0188
		B5032		Measured	08/15/2020 16:14:03	7519020.4492	4698286.1612	652.7820		0.0540
		B5033		Measured	08/15/2020 16:12:44	7519017.3744	4698265.9631	651.9859		0.0949
		RTCM-Ref 0001		Reference	08/15/2020 10:31:47	7515723.9185	4725626.1443	709.2462		0.0000
		RTCM-Ref 0003		Reference	08/15/2020 11:20:31	7503168.9298	4699391.6087	628.0260		0.0000
		RTCM-Ref 0057		Reference	08/15/2020 10:01:42	7519060.0387	4698296.8718	653.0129		0.0000
		RTCM-Ref 0061		Reference	08/15/2020 10:43:08	7518984.6692	4698286.4618	651.4469		0.0000
		RTCM-Ref 0080		Reference	08/15/2020 12:00:07	7519045.4442	4698332.3599	651.5179		0.0000
		RTCM-Ref 0080(1)		Reference	08/24/2020 15:48:52	7519066.8973	4698302.4097	652.5139		0.0000
		RTCM-Ref 0095		Reference	08/24/2020 16:15:07	7519041.4008	4698107.1651	662.6459		0.0000
		RTCM-Ref 0103		Reference	08/24/2020 16:56:14	7518979.0952	4698246.7011	649.6629		0.0000
		RTCM-Ref 0106		Reference	08/15/2020 13:45:17	7519070.8658	4698300.3316	653.9349		0.0000
		RTCM-Ref 0108		Reference	08/15/2020 14:26:27	7519026.7701	4698232.1379	652.0040		0.0000
		RTCM-Ref 0111		Reference	08/15/2020 14:47:27	7519056.6119	4698233.0725	653.6349		0.0000
		RTCM-Ref 0118		Reference	08/15/2020 15:10:21	7519076.2159	4698205.7337	652.8169		0.0000
		RTCM-Ref 0119		Reference	08/15/2020 15:29:27	7519032.5493	4698202.8025	652.5039		0.0000
		RTCM-Ref 0122		Reference	08/15/2020 15:54:07	7518998.7537	4698110.2723	664.0600		0.0000
		RTCM-Ref 0123		Reference	08/15/2020 16:22:32	7519017.5466	4698161.0159	657.2429		0.0000



Republika e Kosovës

Republika Kosova - Republic of Kosovo

Qeveria e Kosovës - Vlada Kosova - Government of Kosovo

Ministria e Infrastrukturës dhe Ambientit/ Ministrastvo Infrastrukture i Sredine/ Ministry of Infrastructure and Environment
AGJENCIJA KADASTRALE E KOSOVËS/ KOSOVSKA KATASTARSKA AGENCIJA/ KOSOVA CADASTRAL AGENCY

GJENDJA E VJETËR / STARO STANJE												GJENDJA E RE / NOVO STANJE						
Nr. rendor, Redni broj	Komuna	Opština	Zona kadastrale	Katastarska zona	Mbiemri, Emri (Emri i Babës) Adresa e vendbanimit Prezime, Ime (Ime Oca) Adresa prebivališta	Nr. personal nga: Personalni Br. iz: 1. Pronar - Vlasnik - Owner 2. Posedues - Posednik - Possessor 3. Shfrytëzues - Korisnik - User	Nr. i Njësisë Br. Jedinice	1. (P) Parcela u/r 2. (O) Ndërtesa u/r Zgrada 3. (O) Pj. e ndërt. u/r Deo Zgrade	Kultura, klasa Shfrytëzimi aktual	□ □ □	Përshkrimi i gjendjes së Njësisë Opis stanja Jedinice	Mbiemri, Emri (Emri i Babës) Adresa e vendbanimit Prezime, Ime (Ime Oca) Adresa prebivališta	Nr. i Njësisë Br. Jedinice	1. (P) Parcela u/r 2. (O) Ndërtesa u/r Zgrada 3. (O) Pj. e ndërt. u/r Deo Zgrade	Kultura, klasa Shfrytëzimi aktual	□ □ □	Sipërfaqja, Površina (m²)	Dokumenti në të cilin bazohet ndërrimi dhe rezultati i shiqimit në vend të ngjarjes nga personi zyrtar përmirëmbajtjen e kadastrit.
1	2	3	4	5	6	7	8	9	10	11	12	13	14					
1	Ferizaj	Rahovicë	1	Bedri (Mejdi) Sylejmani	1	1171039521	1	1949-1 2310-0	Arë(5) Arë(6) Livadh (3)	2218 4387 1846	XHEPSINE	1	Bedri (Mejdi) Sylejmani	1	R	01949-3 01949-4 01949-5 2310-1 2310-2 2310-3 Gjithësej	Arë(5) Arë(5) Arë(5) Arë(6) Livadh (3) Arë(6) Livadh (3) Arë(6) Livadh (3) Gjithësej	810 1251 157 987 189 1873 655 1527 1002 8451
Gjeodeti/kompania e licencuar: LIRIDON SEJDIU				Nr i licencës: 140								Nënshkrimi dhe vula:						



Republika e Kosovës
Republika Kosova-Republic of Kosovo
Geveria e Kosovës- Vlada Kosova- Government of Kosovo
Ministria e Infrastrukturës dhe Ambientit/ Ministratvo Infrastrukture i Sredine/ Ministry of Infrastructure and Environment
AGJENCIJA KADASTRALE E KOSOVËS/KOSOVSKA KATASTARSKA AGENCIJA/ KOSOVO CADASTRAL AGENCY

Komuna: Ferizaj	Zona Kadastrale: Rahovicë
Numri i njësisë kadastrale: 1949-1,2310-0	Sistemi koordinat: KosovaRef01

Nr	Y	X	H	Kodi	Përshkrimi	Burimi
220086	7512362.388	4694374.660	620.669	11	Monoment	PM
5001	7519006.922	4698108.252	664.614	1	Guri	PM
5016	7519047.188	4698104.222	664.935	-	-	PM
5031	7519004.544	4698286.160	651.921	2	Kunjë - shtyllë metalike	PM
38876	7518959.738	4698282.408	648.955	1	Guri	PM
38879	7519020.438	4698286.115	652.782	1	Guri	PM
38884	7519076.146	4698227.376	653.897	2	Kunjë - shtyllë metalike	PM
38885	7519063.256	4698232.446	654.200	-	-	PM
38889	7519031.706	4698235.117	0.000	2	Kunjë - shtyllë metalike	PM
38890	7519013.766	4698238.238	651.080	2	Kunjë - shtyllë metalike	PM
38891	7519017.407	4698265.946	652.013	2	Kunjë - shtyllë metalike	PM
38894	7519026.305	4698204.809	652.261	1	Guri	PM
38902	7519018.253	4698162.481	657.720	1	Guri	PM
38938	7519004.914	4698240.543	650.257	2	Kunjë - shtyllë metalike	PM
38942	7518983.720	4698246.630	0.000	2	Kunjë - shtyllë metalike	PM
38951	7518958.517	4698256.320	648.129	-	-	PM
48053	7519079.990	4698224.900	653.868	2	Kunjë - shtyllë metalike	PM
48054	7519075.770	4698205.150	653.661	-	-	PM
48055	7519068.220	4698166.790	656.106	1	Guri	PM
48056	7519062.230	4698137.550	661.318	1	Guri	PM
48057	7519055.380	4698101.950	666.265	1	Guri	PM
48058	7519071.732	4698184.635	653.852	1	Guri	PM
7	7519017.411	4698286.124	652.594	2	Kunjë - shtyllë metalike	PM
9	7519010.100	4698239.193	650.501	2	Kunjë - shtyllë metalike	PM
10	7519036.788	4698234.528	652.016	2	Kunjë - shtyllë metalike	PM
20	7519054.309	4698226.785	652.697	2	Kunjë - shtyllë metalike	PM
21	7519052.107	4698227.006	652.656	2	Kunjë - shtyllë metalike	PM
40	7519042.092	4698104.732	664.847	2	Kunjë - shtyllë metalike	PM
43	7519020.859	4698106.857	664.619	2	Kunjë - shtyllë metalike	PM
48	7518986.361	4698284.637	650.722	2	Kunjë - shtyllë metalike	PM
38888	7519052.676	4698232.686	652.805	2	Kunjë - shtyllë metalike	PM
38950	7518983.555	4698248.467	649.565	2	Kunjë - shtyllë metalike	PM

Matja e pikave në dy seri						
Seria	Nr. Pikës	Y	X	H	ΔY	ΔX
I	5001	7519006.92	4698108.25	664.61	-0.0340	-0.0140
II	5001	7519006.96	4698108.27	664.60		0.0368
I	38894	7519026.306	4698204.817	652.26	-0.0140	0.0240
II	38894	7519026.32	4698204.793	652.46		0.0278
I	38902	7519018.28	4698162.48	657.64	0.0130	-0.0190
II	38902	7519018.27	4698162.50	657.72		0.0230
I	38879	7519020.449	4698286.13	652.76	0.0000	-0.0310
II	38879	7519020.449	4698286.161	652.78		0.0310
I	38891	7519017.386	4698265.943	652.0129	0.0120	-0.0200
II	38891	7519017.374	4698265.963	651.9859		0.0233

Koordinatat përfundimtare			
Nr	Y	X	H
5001	7519006.939	4698108.259	664.607
38894	7519026.313	4698204.805	652.360
38902	7519018.274	4698162.488	657.681
38879	7519020.449	4698286.146	652.770
38891	7519017.380	4698265.953	651.999

Gjeodeti / Kompania gjeodete e licencuar:	Liridon Sejdiu	Nënshkrimi dhe vula:	
Numri i licencës	140		



Republika e Kosovës
Republika Kosova-Republic of Kosovo
Qeveria e Kosovës- Vlada Kosova- Government of Kosovo

Ministria e Infrastrukturës dhe Ambientit/ Ministrastvo Infrastrukture i Sredine/ Ministry of Infrastructure and Environment

AGJENCIA KADASTRALE E KOSOVËS/KOSOVSKA KATASTARSKA AGENCIJA/ KOSOVO CADASTRAL AGENCY

FORMULARI PËR KORIGJIMIN E SIPËRFAQËS

Gjeodeti / Kompania gjeodete e licencuar: Liridon Sejdiu	Numri i licencës:140
Komuna: Ferizaj	Zona Kadastrale: Rahovicë
Numri i njësisë kadastrale: 00288-0	Numri i lëndës: 163/2020

1. Tabela e ndryshimeve të sipërfaqes

Numri i parcelës	Sipërfaqja faktike (m ²)	Sipërfaqja nga SIKTK-T (m ²)	Ndryshimi (m ²)	Sipërfaqja e korrigjuar (m ²)
01949-1	2218	2212	6	2218

Bazuar në procesverbalin e terrenit, pronarët janë pajtuar me pikat definitive kufitare të vendosura në terren nga të cilat edhe është derivuar sipërfaqja definitive që regjistrohet në SIKTK.

Nënshkrimi dhe vula e gjodetit: _____

Data: _____



Republika e Kosovës
Republika Kosova-Republic of Kosovo
Qeveria e Kosovës- Vlada Kosova- Government of Kosovo

Ministria e Infrastrukturës dhe Ambientit/ Ministrastvo Infrastrukture i Sredine/ Ministry of Infrastructure and Environment

AGJENCIA KADASTRALE E KOSOVËS/KOSOVSKA KATASTARSKA AGENCIJA/ KOSOVO CADASTRAL AGENCY

RAPORTI TEKNIK

Gjeodeti / Kompania gjeodete e licencuar: Liridon Sejdiu	Numri i licencës: 140
Komuna: Ferizaj	Zona Kadastrale: Rahovicë
Numri i njësisë kadastrale: 01949-1,2310-0	Lloji i lëndës: Ndarje e parcelës

Bazuar në kërkesën e palës **Bedri (Mejdi) Sylejmani** me numër personal **1171039521** të parashtuar me datën **13/08/2020**, është bërë kërkesa për marrjen e produkteve kadastrale në Zyrën Kadastrale Komunale **Ferizaj** me datë **14/08/2020**.

Pas analizimit të dhënave me datë **15/08/2020** janë realizuar matjet në terren, për (**ndarjen/bashkimin**) e parcelave bazuar në (**gjendjen faktike/sipërfaqe të barazuara**).

Matjet në terren janë realizuar me instrument (GPS Leica 1230), ku fillimisht është bërë matja e pikës kontrolluese **22086** pastaj matjet janë realizuar bazuar në kornizën AKK nr.: 2020/01

Matje të dyfishta kontrolluese janë realizuar në pikat numër **5001,38894,38902,38879,38891**

Sfidat gjatë realizimit të

matjeve: _____

Matje të dyfishta kontrolluese janë realizuar në pikat numër **5001,38894,38902,38879,38891**.

Raporti në formë tabelare:

Parcela para ndarjes/bashkimit	Sipërfaqja (m ²)	Korigjimi i sipërfaqe (po/jo)	Parcela pas ndarjes/bashkimit	Sipërfaqja (m ²)
01949-1	2218	po	01949-3	810
			01949-4	1251
			01949-5	157
2310-0	6233	jo	2310-1	509
			2310-2	2528
			2310-3	3196

Nënshkrimi dhe vula e gjodetit: _____

Data: _____



Republika e Kosovës
Republika Kosova-Republic of Kosovo
Qeveria - Vlada - Government

MINISTRIA E EKONOMISË DHE AMBIENTIT / MINISTARSTVO EKONOMIJE I ŽIVOTNE SREDINE / MINISTRY OF ECONOMY AND ENVIRONMENT
AGJENCIA KADASTRALE E KOSOVËS / KATASTARSKA AGENCIJA KOSOVA / KOSOVO CADASTRAL AGENCY

CERTIFIKATË / CERTIFIKAT / CERTIFICATE

PERSONI / OSOBA / PERSON : SYLEJMANI BEDRI

Numri i lëndës / Broj Predmet / Case Referent Number:	67377-2020
Data dhe koha e lëshimit / Datum i vreme izdavanja / Date and time of submission:	24.08.2020 - 09:33
Komuna / Opština / Municipality:	Ferizaj / Uroševac / Ferizaj
Zyra Kadastrale Komunale / Opštinska Katastarska Kancelarija / Municipal Cadastral Office:	Ferizaj / Uroševac / Ferizaj

A. TË DHËNAT PËR PERSONIN / PODACI O OSOBI / PERSON'S DATA

Mbiemri/Emri i afarizmit (biznesit) Prezime/ Naziv poslovanja (biznisa) Last Name / Business Name	Emri Ime First Name	Emri i babait Ime oca Father's Name	Gjinia Pol Gender	Nr. personal/ biznesit Lični broj/broj poslovanja ID. No.	Shteti i shtetësisë apo regjistrimit Država državljanstva ili uknjiženja Country of citizenship	Ditëlindja/Data e themelimit Rodendan/Dan osnivanja Date of Birth/Establishmen t	Krijuar më datën Uradjeno na dan Created On	Azhuruar Ažurirano Updated
SYLEJMANI	BEDRI	MEJDI	Mashkull / Musko / Male	1171039521	KOSOVA / KOSOVA / KOSOVO	15.05.1957		07.11.2014

A.1 ADRESA E PERSONIT / ADRESA OSOBE / PERSON'S ADDRESS

Vendbanimi Prebivaliste Resident	Kodi Postal Poštanski Kod Postal Code	Hollësitë e adresës Pojedinosti adrese Address Details	Adresa tjetër Druga adresa Other address	Azhuruar Ažurirano Updated
RAHOVICE / RAHOVICE / RAHOVICE		"ESAT MEKULI"	FERIZAJ	07.11.2014



B. NJESIA KADASTRALE/ KATASTARSKA JEDINICA/CADASTRAL UNIT

Njësia kadastrale Katastarska jedinica Cadastral unit	Komuna / Opština / Municipality	Zona kadastrale Katastarska zona Cadastral zone	Lloji i njësisë Vrsta jedinice Unit type	Tipi i pronës Tip imovine Property Type / Lloji i pronës Vrsta imovine Property kind	Kati/ Katet Br.Sprat a/ Spratova Floor number	Vendi i quajtur Zvano mesto Place name	Sipërfaqja Površina Area	Shfrytezimi aktual/Kultura- klasa Aktuelna upotreba/ Kultura-klasa Actual use/Culture-class	Pjesa e pronës Deo imovine Share quota	Lloji i së drejtës Vrsta prava Type of the right	Azhuruar Ažurirano Updated
P-72217072-01712-1	Ferizaj / Uroševac / Ferizaj	RAHOVICË / RAHOVICA / RAHOVICË	PARCELË / PARCELA / parcel	/ R		XHELPSINA / XHELPSINA / XHELPSINA	4373	Bujqësore - Arat - Arë E Klasës 6 / / Poljoprivredno - Njive - Njiva 6 Klase / / Agriculture - Arable - 6th Class Arable Land / /	1 / 1	Posedim individual / Individualna Drzavina / single possessor	20.08.2018
P-72217072-01713-1	Ferizaj / Uroševac / Ferizaj	RAHOVICË / RAHOVICA / RAHOVICË	PARCELË / PARCELA / parcel	/ R		XHELPSINA / XHELPSINA / XHELPSINA	1878	Bujqësore - Livadhet - Livadh I Klasës 3 / / Poljoprivredno - Livade - Livada 3 Klase / / Agriculture - meadow - 3rd Class Meadow / /	1 / 1	Posedim individual / Individualna Drzavina / single possessor	20.08.2018
P-72217072-01949-1	Ferizaj / Uroševac / Ferizaj	RAHOVICË / RAHOVICA / RAHOVICË	PARCELË / PARCELA / parcel	Pronë private Privatna Imovina Privately owned Land / R		XHELPSINA / XHELPSINA / XHELPSINA	2212	Bujqësore - Arat - Arë E Klasës 5 / / Poljoprivredno - Njive - Njiva 5 Klase / / Agriculture - Arable - 5th Class Arable Land / /	1 / 1	Posedim individual / Individualna Drzavina / single possessor	14.06.2016